


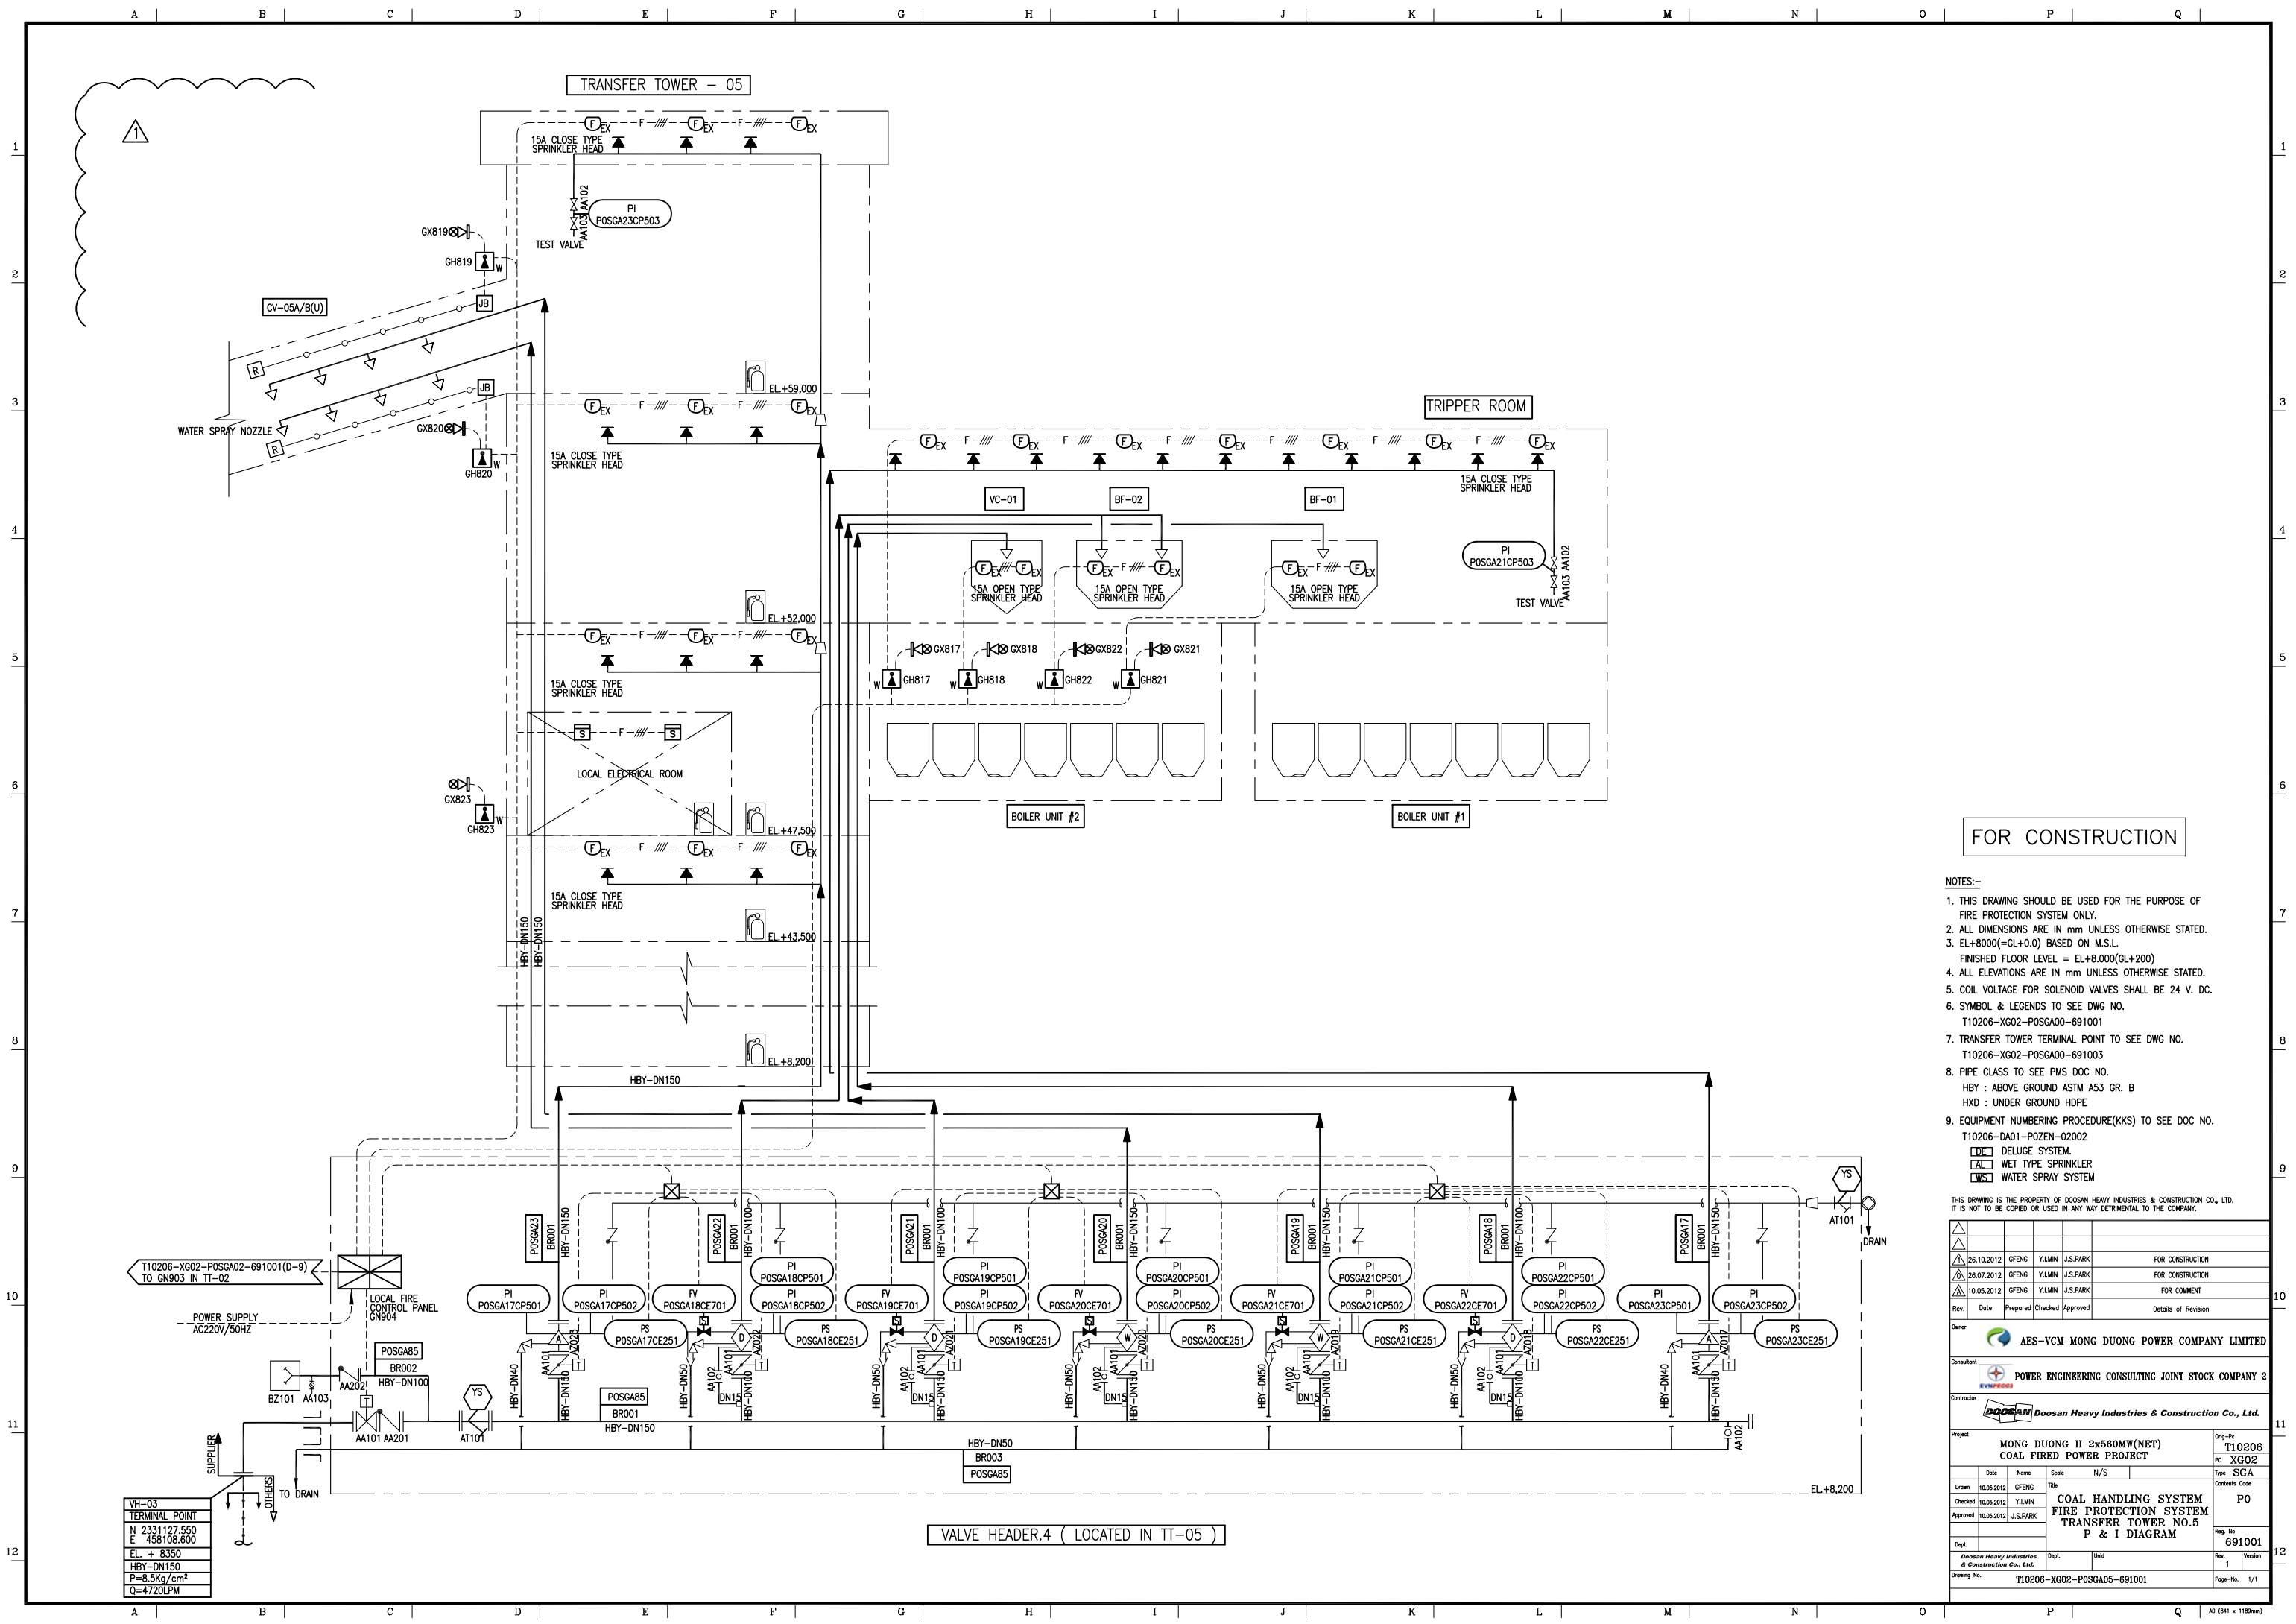

FOR CONSTRUCTION

- NOTES:-
1. THIS DRAWING SHOULD BE USED FOR THE PURPOSE OF FIRE PROTECTION SYSTEM ONLY.
 2. ALL DIMENSIONS ARE IN mm UNLESS OTHERWISE STATED.
 3. EL+8000(=GL+0.0) BASED ON M.S.L.
FINISHED FLOOR LEVEL = EL+8.000(GL+200)
 4. ALL ELEVATIONS ARE IN mm UNLESS OTHERWISE STATED.
 5. COIL VOLTAGE FOR SOLENOID VALVES SHALL BE 24 V. DC.
 6. SYMBOL & LEGENDS TO SEE DWG NO. T10206-XG02-POSGA00-691001
 7. TRANSFER TOWER TERMINAL POINT TO SEE DWG NO. T10206-XG02-POSGA00-691003
 8. PIPE CLASS TO SEE PMS DOC NO. T10206-DA01-POZEN-02002
 9. EQUIPMENT NUMBERING PROCEDURE(KKS) TO SEE DOC NO. T10206-DA01-POZEN-02002
- DE DELUGE SYSTEM.
AI WET TYPE SPRINKLER
WS WATER SPRAY SYSTEM

THIS DRAWING IS THE PROPERTY OF DOOSAN HEAVY INDUSTRIES & CONSTRUCTION CO., LTD. IT IS NOT TO BE COPIED OR USED IN ANY WAY DETRIMENTAL TO THE COMPANY.

					
	26.10.2012	GFENG	Y.L.MIN	J.S.PARK	FOR CONSTRUCTION
	26.07.2012	GFENG	Y.L.MIN	J.S.PARK	FOR CONSTRUCTION
	10.05.2012	GFENG	Y.L.MIN	J.S.PARK	FOR COMMENT
Rev.	Date	Prepared	Checked	Approved	Details of Revision
Owner					
 AES-VCM MONG DUONG POWER COMPANY LIMITED					
Consultant					
 POWER ENGINEERING CONSULTING JOINT STOCK COMPANY 2					
Contractor					
 Doosan Heavy Industries & Construction Co., Ltd.					
Project					Orig.-No.
MONG DUONG II 2x560MW(NET)					T10206
COAL FIRED POWER PROJECT					PC XG02
	Date	Name	Scale	N/S	Type SGA
Drawn	10.05.2012	GFENG			Contents Code
Checked	10.05.2012	Y.L.MIN			P0
Approved	10.05.2012	J.S.PARK			
Dept.				Unit	Reg. No.
Doosan Heavy Industries & Construction Co., Ltd.					691001
					Rev.
					1
					Version
Drawing No.					Page-No.
T10206-XG02-POSGA05-691001					1/1