


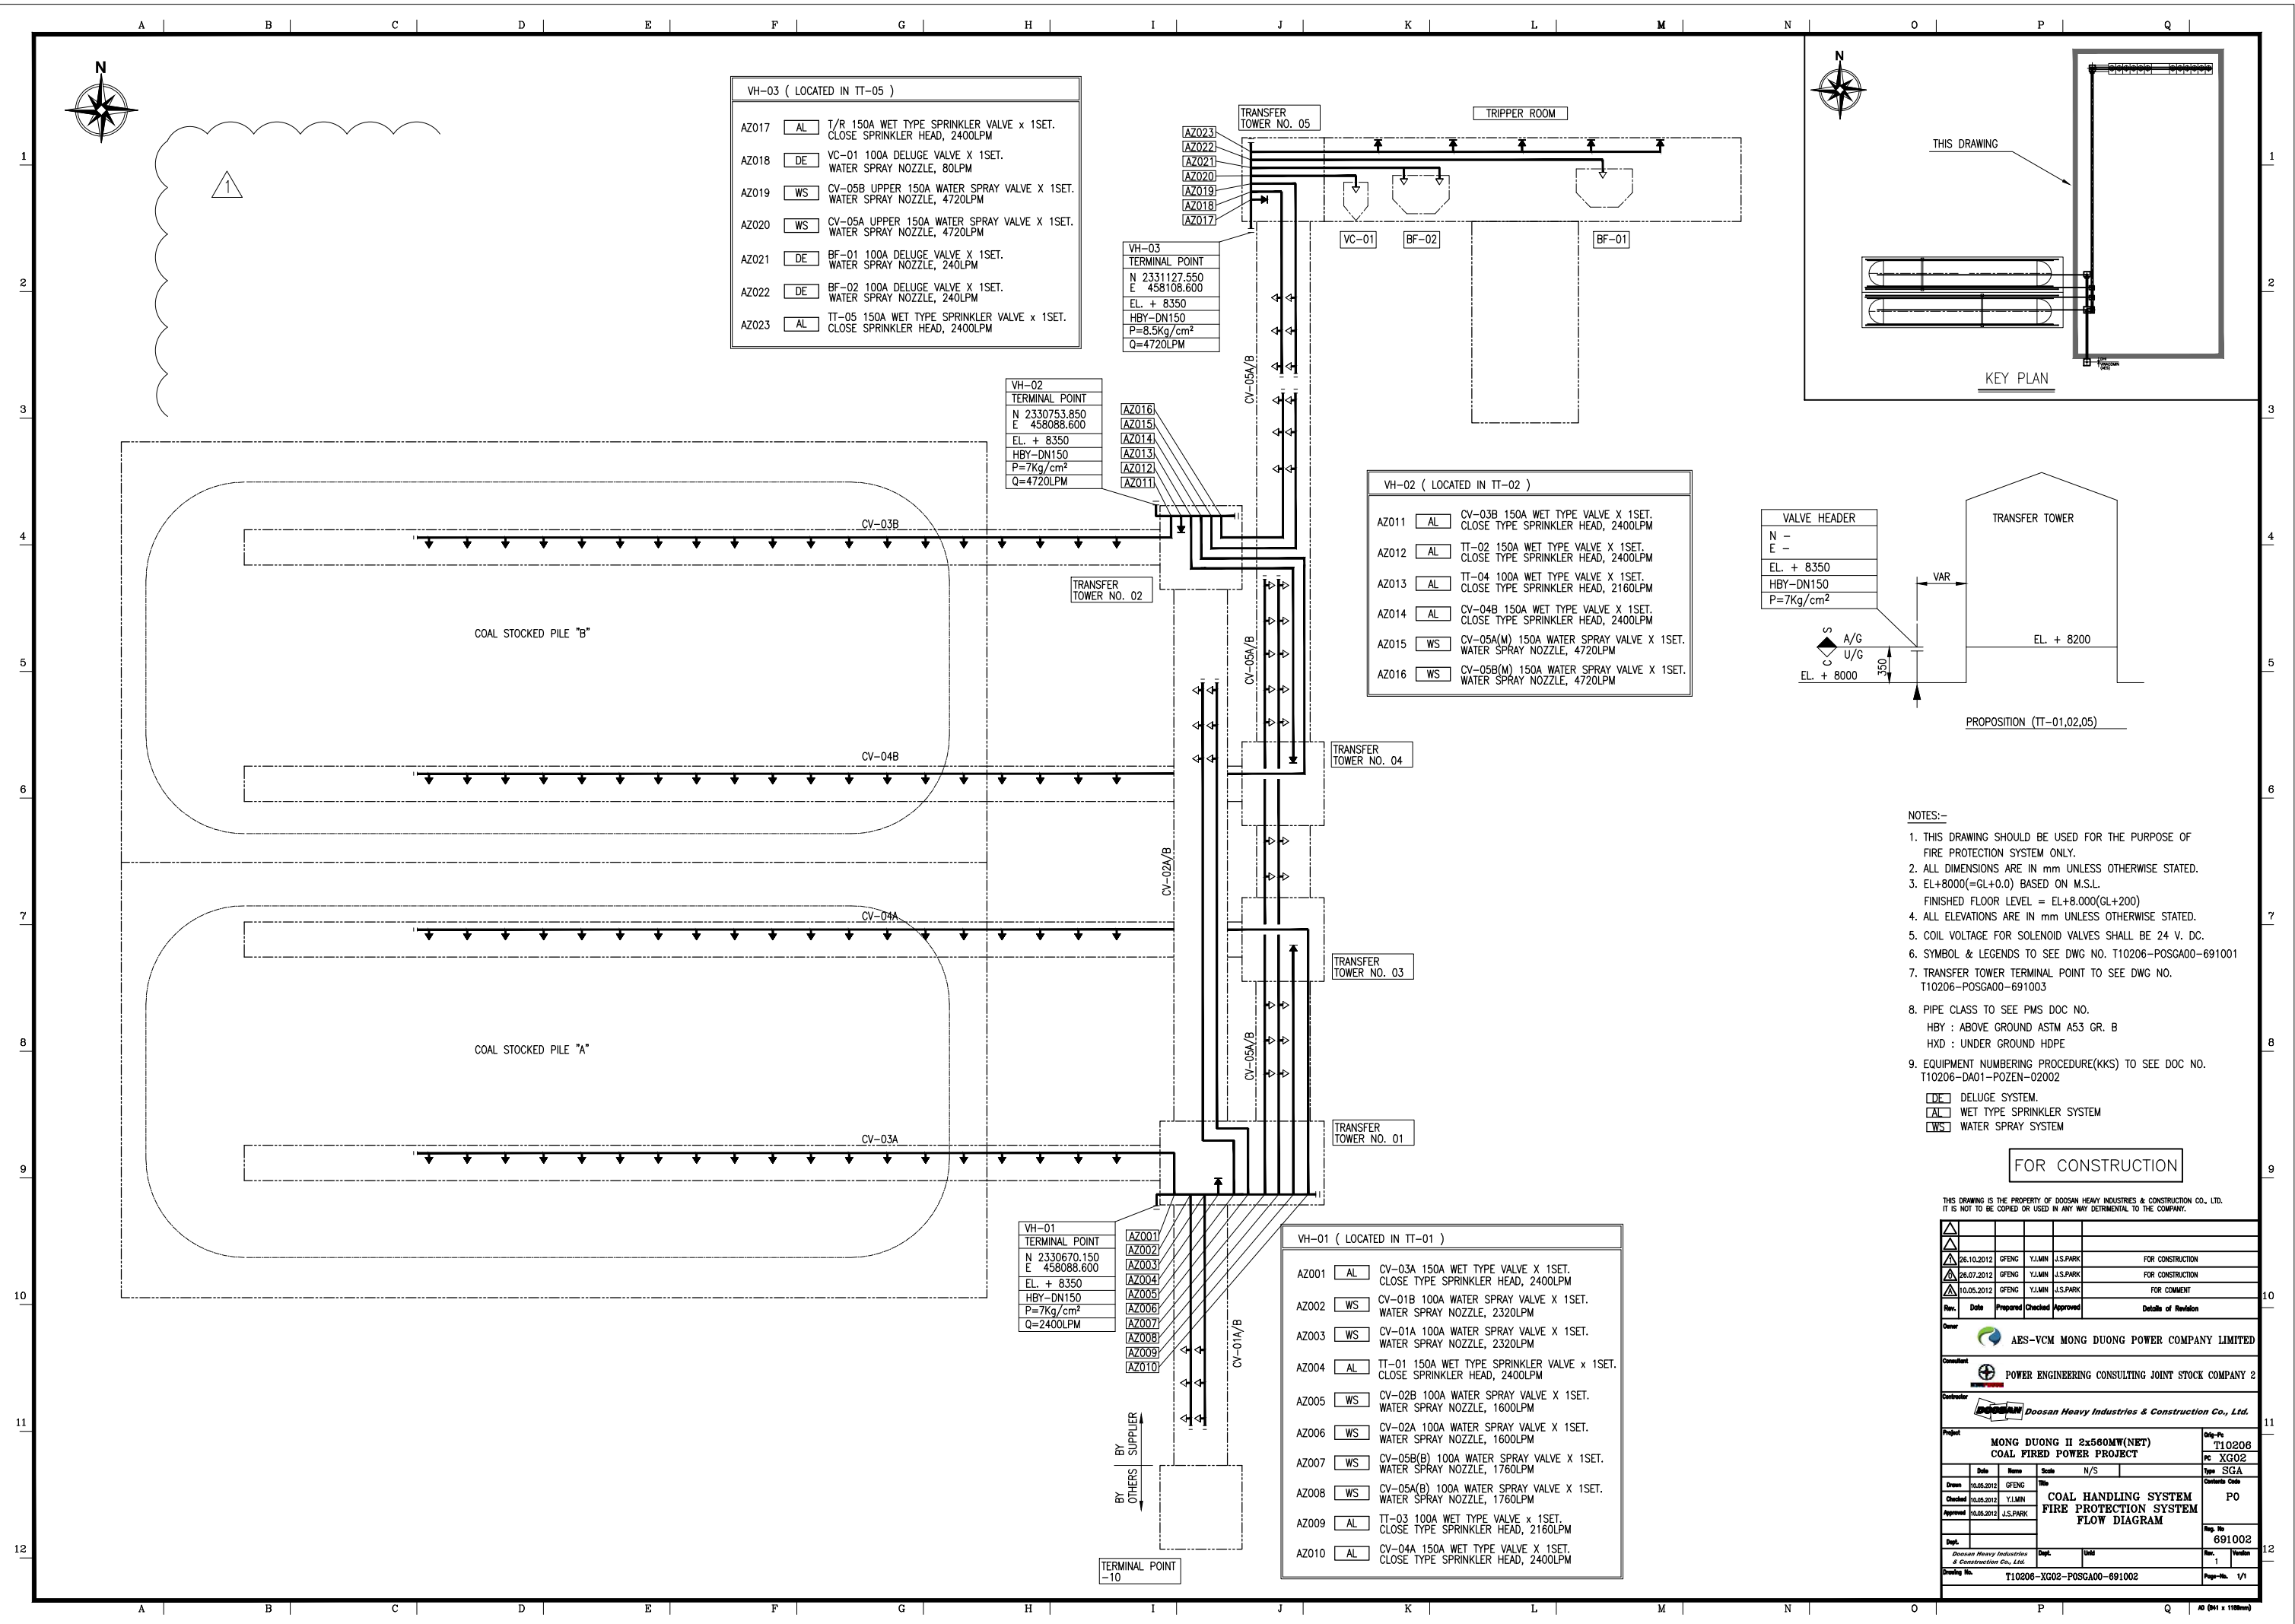

THIS DRAWING IS THE PROPERTY OF DOOSAN HEAVY INDUSTRIES & CONSTRUCTION CO., LTD. IT IS NOT TO BE COPIED OR USED IN ANY WAY DETRIMENTAL TO THE COMPANY.									
▲ ▲ ▲ ▲ 26.10.2012 GFENG Y.LMIN J.S.PARK FOR CONSTRUCTION 26.07.2012 GFENG Y.LMIN J.S.PARK FOR CONSTRUCTION 10.05.2012 GFENG Y.LMIN J.S.PARK FOR COMMENT									
Rev.	Date	Prepared	Checked	Approved	Details of Revision				
Owner  AES-VCM MONG DUONG POWER COMPANY LIMITED									
Consultant  POWER ENGINEERING CONSULTING JOINT STOCK COMPANY 2									
Contractor  Doosan Heavy Industries & Construction Co., Ltd.									
Project					Title				
MONG DUONG II 2x560MW(NET) COAL FIRED POWER PROJECT					T10206 FC XG02				
Drawn					Type				
10.05.2012 GFENG					SGA				
Checked					Contents Code				
10.05.2012 Y.LMIN					P0				
10.05.2012 J.S.PARK									
Title					Scale				
COAL HANDLING SYSTEM FIRE PROTECTION SYSTEM FLOW DIAGRAM					N/S				
Sheet					Rep. No.				
1					691002				
Owner					Drawing No.				
Doosan Heavy Industries & Construction Co., Ltd.					T10206-XG02-POSGA00-691002				
Sheet					Page-No.				
1					1/1				