


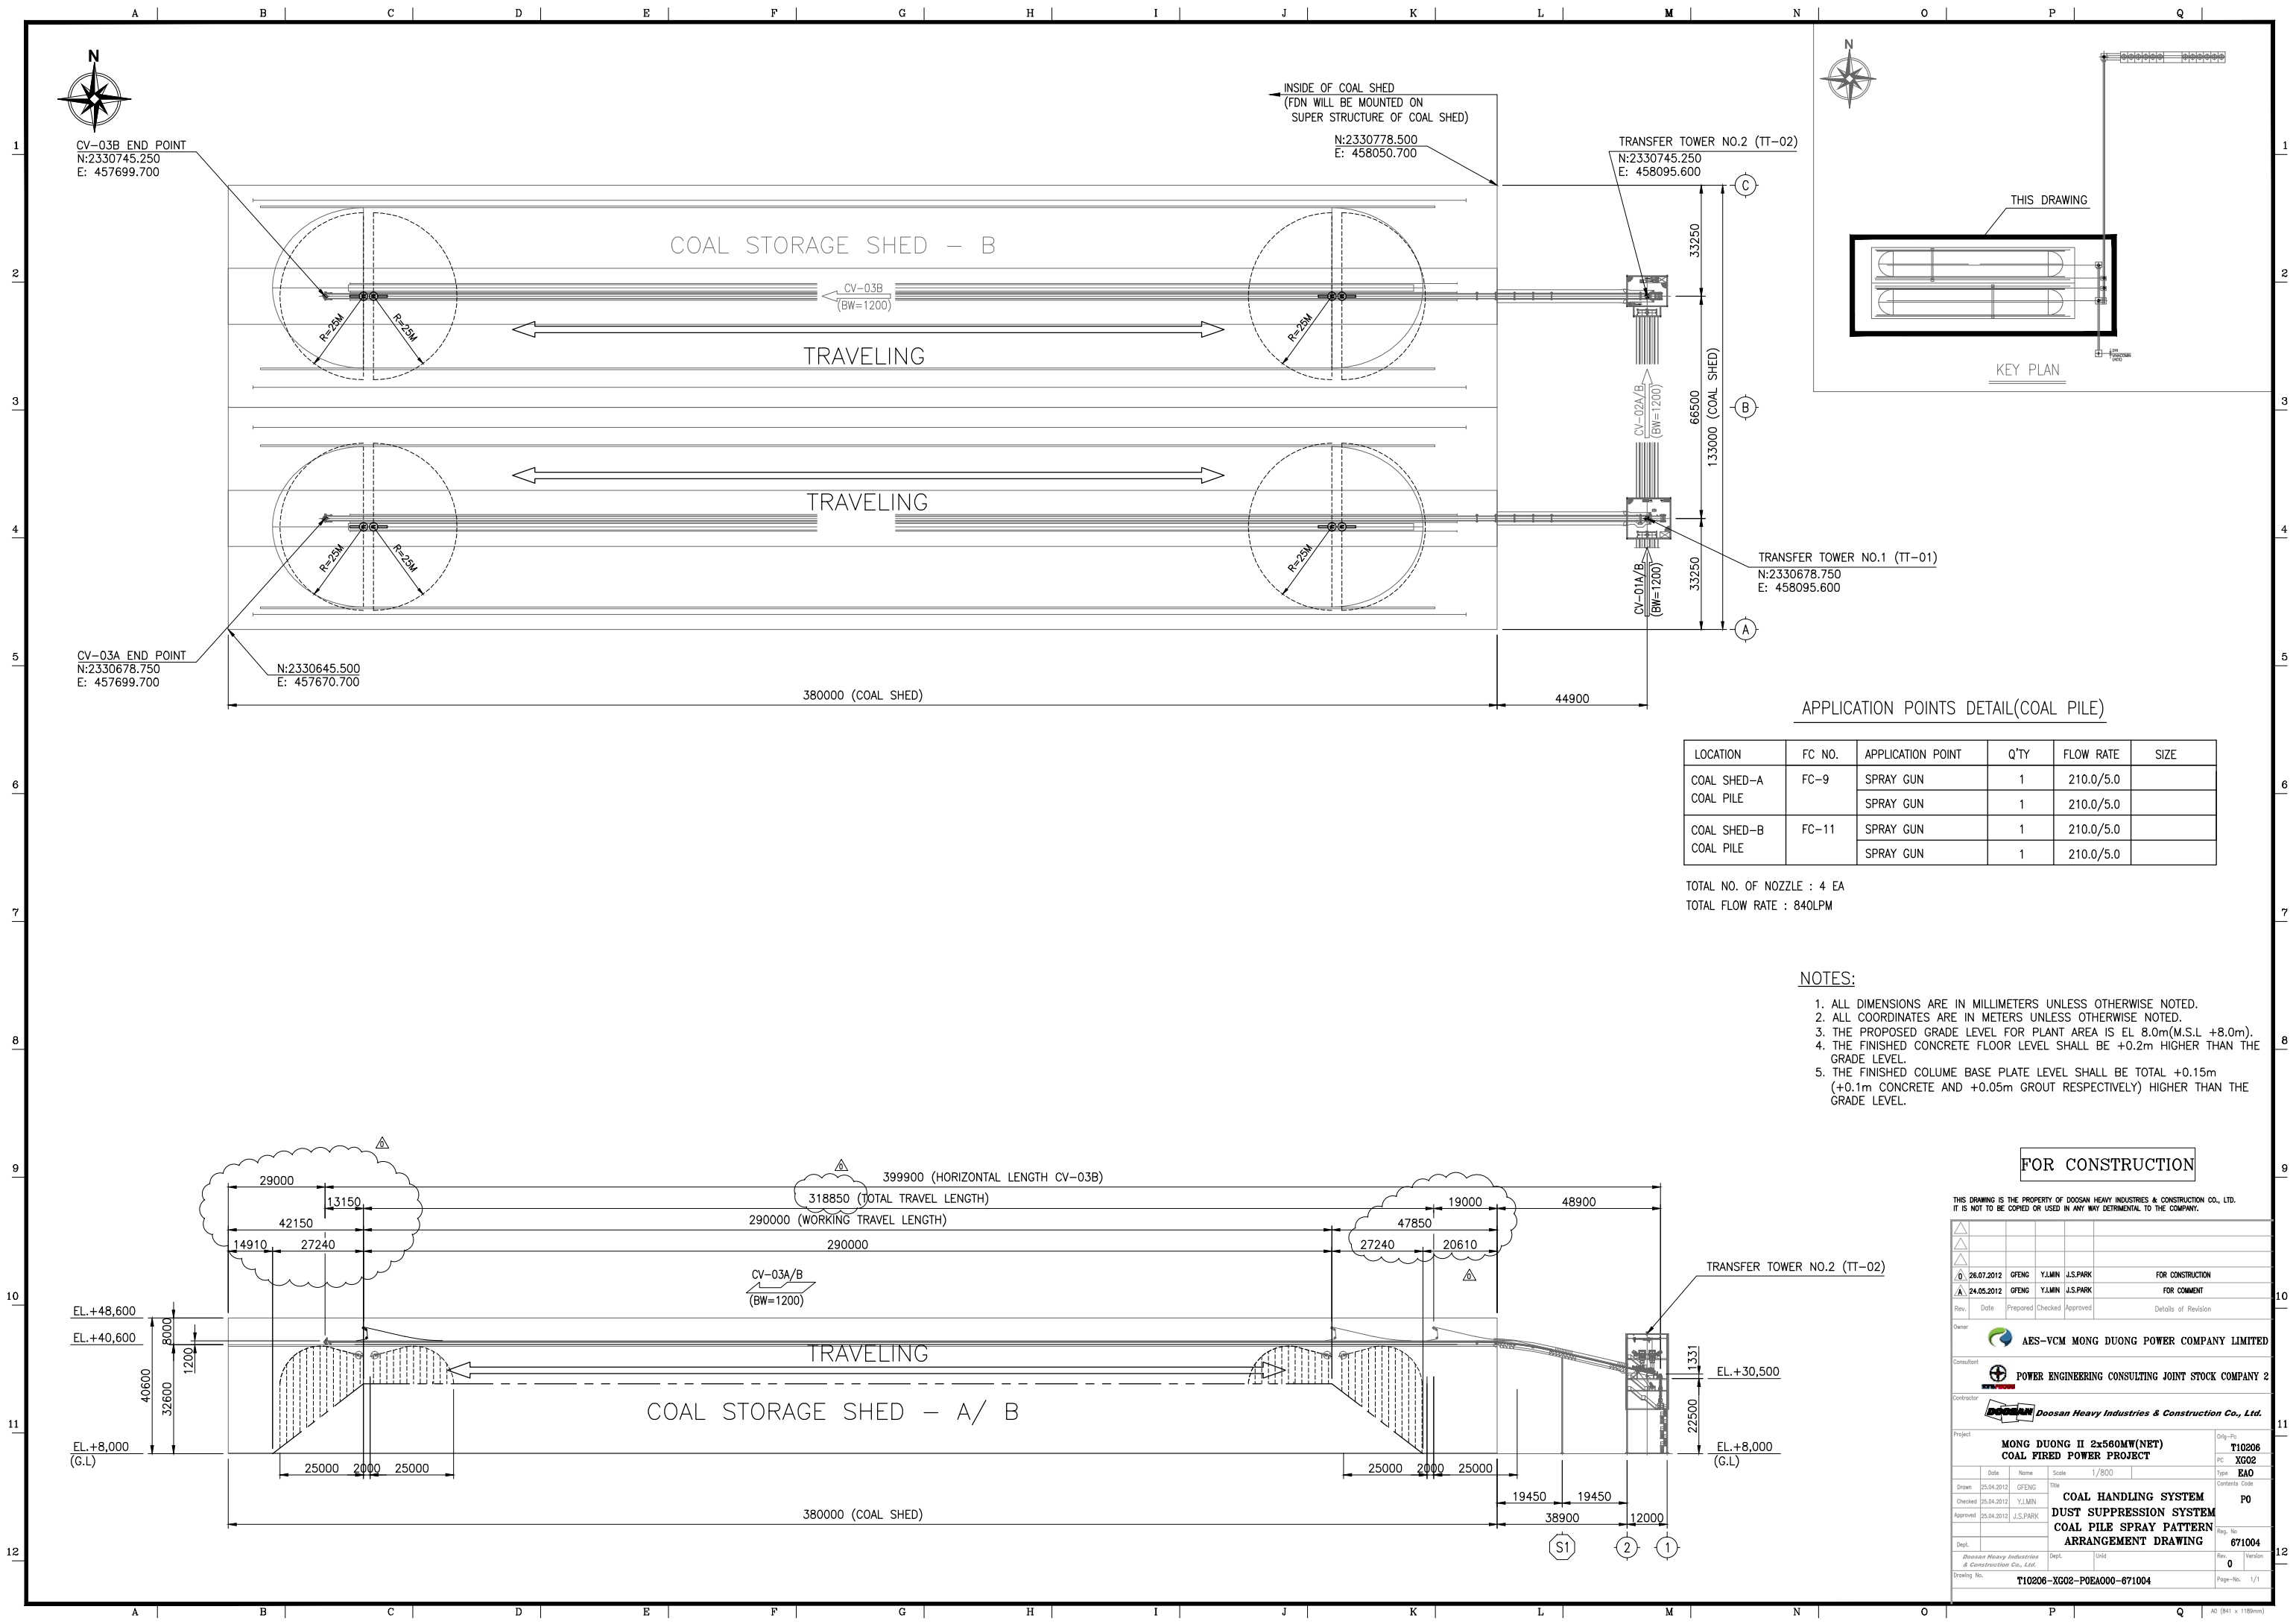

APPLICATION POINTS DETAIL(COAL PILE)

LOCATION	FC NO.	APPLICATION POINT	Q'TY	FLOW RATE	SIZE
COAL SHED-A COAL PILE	FC-9	SPRAY GUN	1	210.0/5.0	
		SPRAY GUN	1	210.0/5.0	
COAL SHED-B COAL PILE	FC-11	SPRAY GUN	1	210.0/5.0	
		SPRAY GUN	1	210.0/5.0	

TOTAL NO. OF NOZZLE : 4 EA
TOTAL FLOW RATE : 840LPM

- NOTES:
1. ALL DIMENSIONS ARE IN MILLIMETERS UNLESS OTHERWISE NOTED.
 2. ALL COORDINATES ARE IN METERS UNLESS OTHERWISE NOTED.
 3. THE PROPOSED GRADE LEVEL FOR PLANT AREA IS EL 8.0m(M.S.L +8.0m).
 4. THE FINISHED CONCRETE FLOOR LEVEL SHALL BE +0.2m HIGHER THAN THE GRADE LEVEL.
 5. THE FINISHED COLUME BASE PLATE LEVEL SHALL BE TOTAL +0.15m (+0.1m CONCRETE AND +0.05m GROUT RESPECTIVELY) HIGHER THAN THE GRADE LEVEL.

FOR CONSTRUCTION

THIS DRAWING IS THE PROPERTY OF DOOSAN HEAVY INDUSTRIES & CONSTRUCTION CO., LTD.
IT IS NOT TO BE COPIED OR USED IN ANY WAY DETRIMENTAL TO THE COMPANY.

Rev.	Date	Prepared	Checked	Approved	Details of Revision
△	26.07.2012	GFENG	YJ.MIN	J.S.PARK	FOR CONSTRUCTION
△	24.05.2012	GFENG	YJ.MIN	J.S.PARK	FOR COMMENT

Owner
AES-VCM MONG DUONG POWER COMPANY LIMITED

Consultant
POWER ENGINEERING CONSULTING JOINT STOCK COMPANY 2

Contractor
Doosan Heavy Industries & Construction Co., Ltd.

Project
MONG DUONG II 2x560MW(NET)
COAL FIRED POWER PROJECT

Only-File
T10206
PC
XG02
Type
EAO

Drawn
25.04.2012
GFENG

Checked
25.04.2012
YJ.MIN

Approved
25.04.2012
J.S.PARK

Scale
1/800

File
COAL HANDLING SYSTEM
DUST SUPPRESSION SYSTEM
COAL PILE SPRAY PATTERN
ARRANGEMENT DRAWING

Reg. No
671004

Dept.
Doosan Heavy Industries
& Construction Co., Ltd.

Unit
0

Version
0

Drawing No.
T10206-XG02-POEA000-671004

Page-No.
1/1